



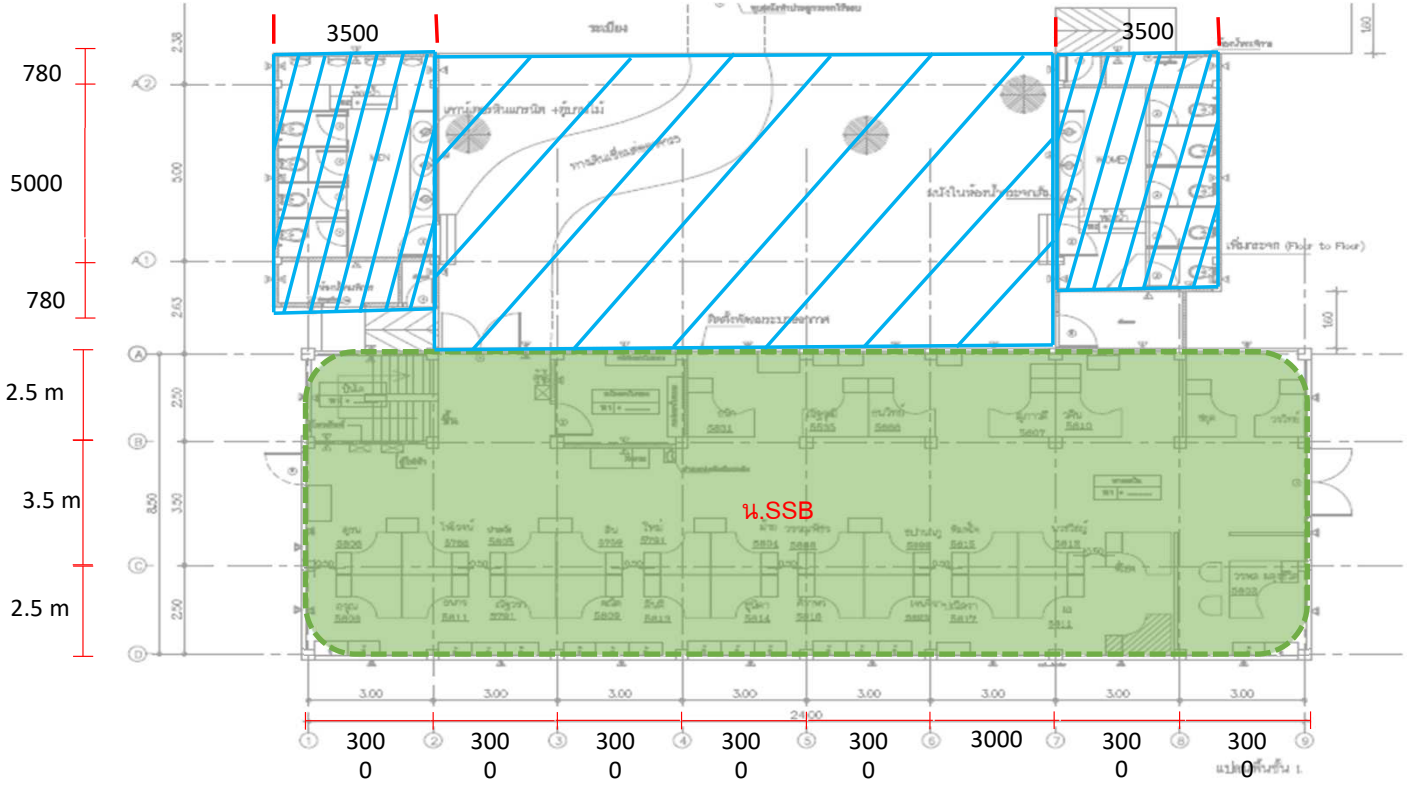


CPAC

อาคาร Riverside 1 ชั้น 1 - หน่วยงาน SSB
- พื้นที่ Office = 204 ตร.ม.

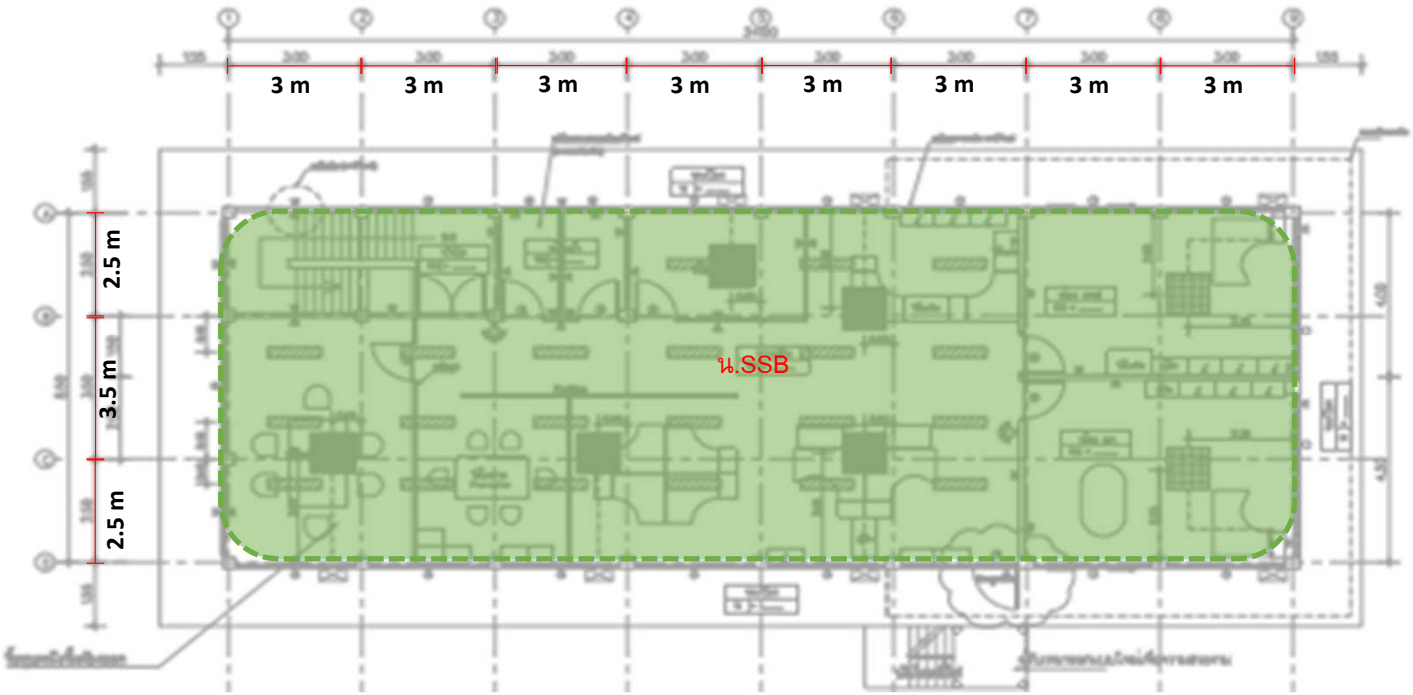

CPAC

อาคาร Riverside 1 ชั้น 2 - หน่วยงาน SSB
- พื้นที่ Office = 204 ตร.ม.

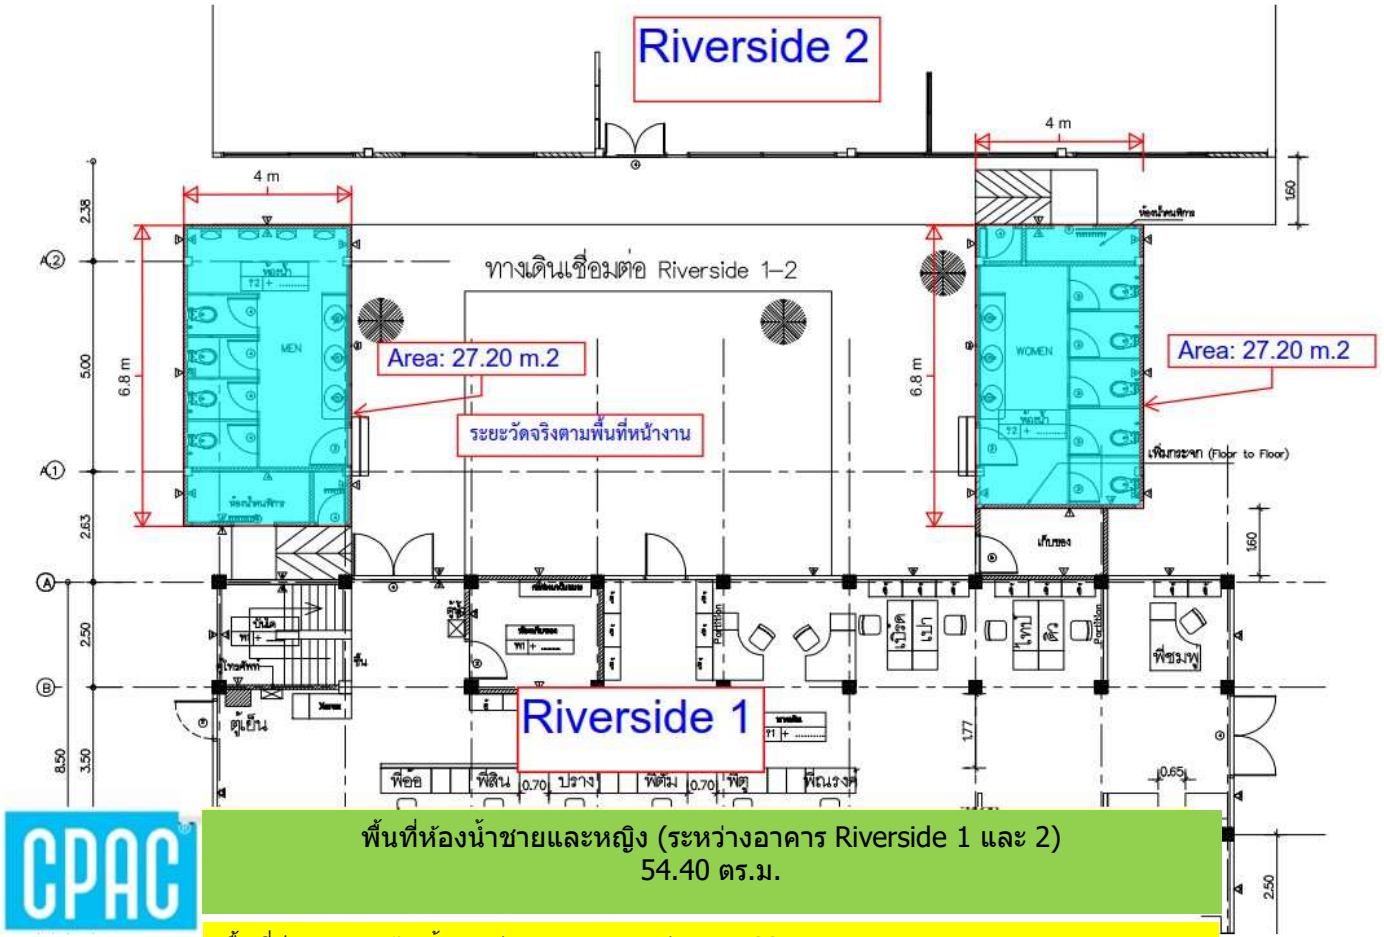

หมายเหตุ ปี 2569 วัดพื้นที่ห้องน้ำใหม่ คำนวณเฉพาะห้องน้ำ ไม่คำนวณพื้นที่ลานชมพู ปรึกษากับพี่เป้ 24.3.68